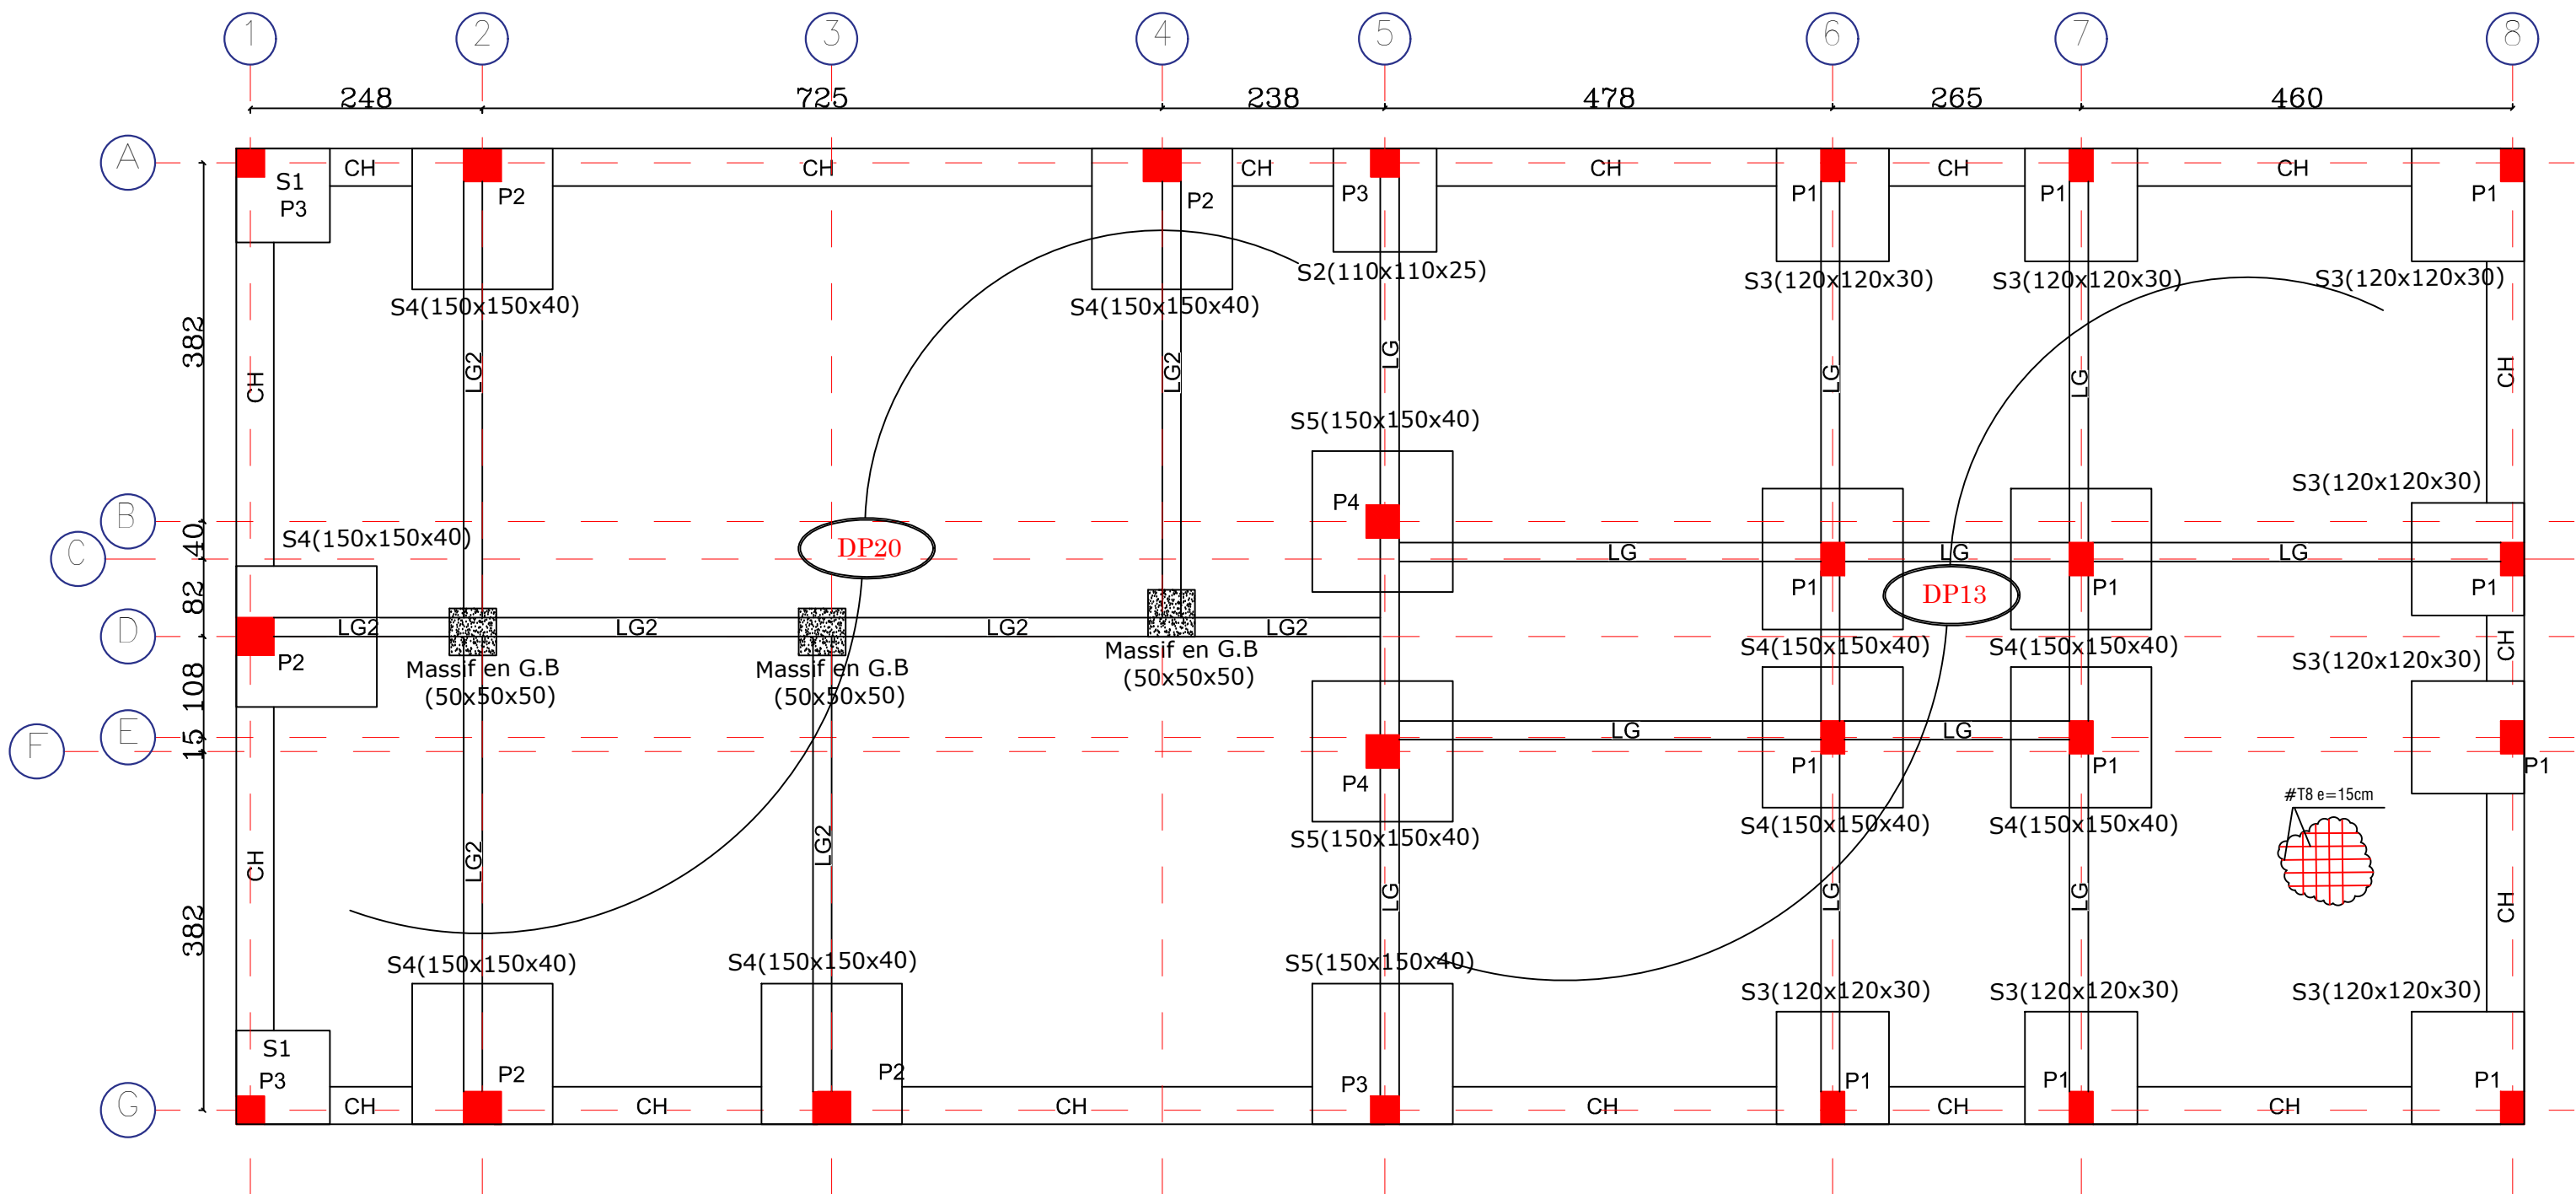
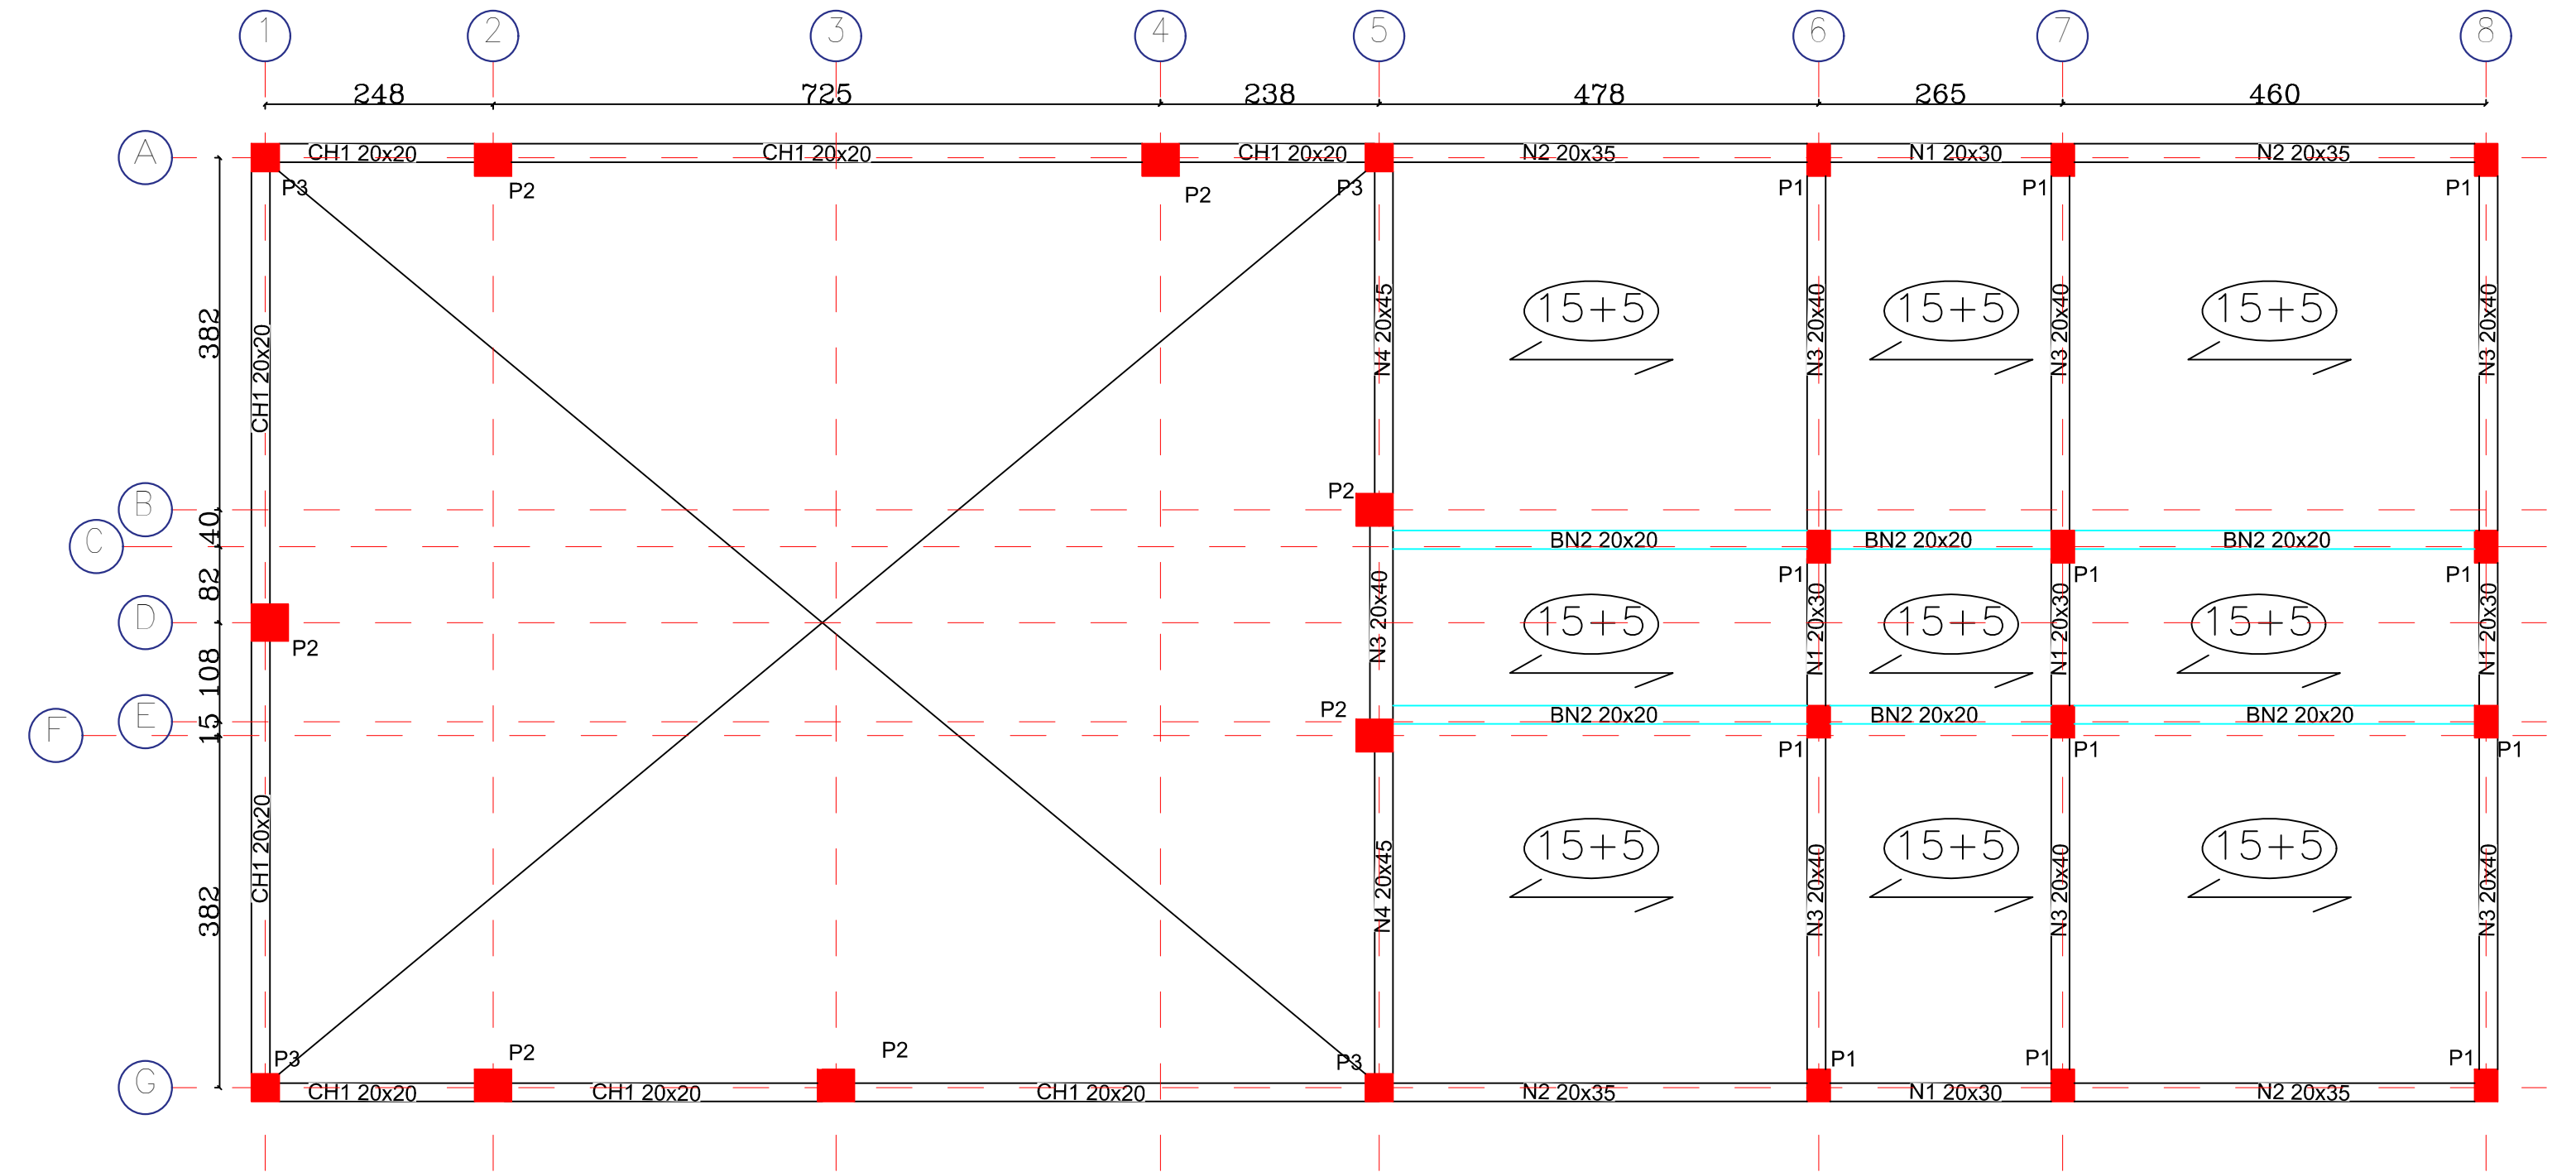






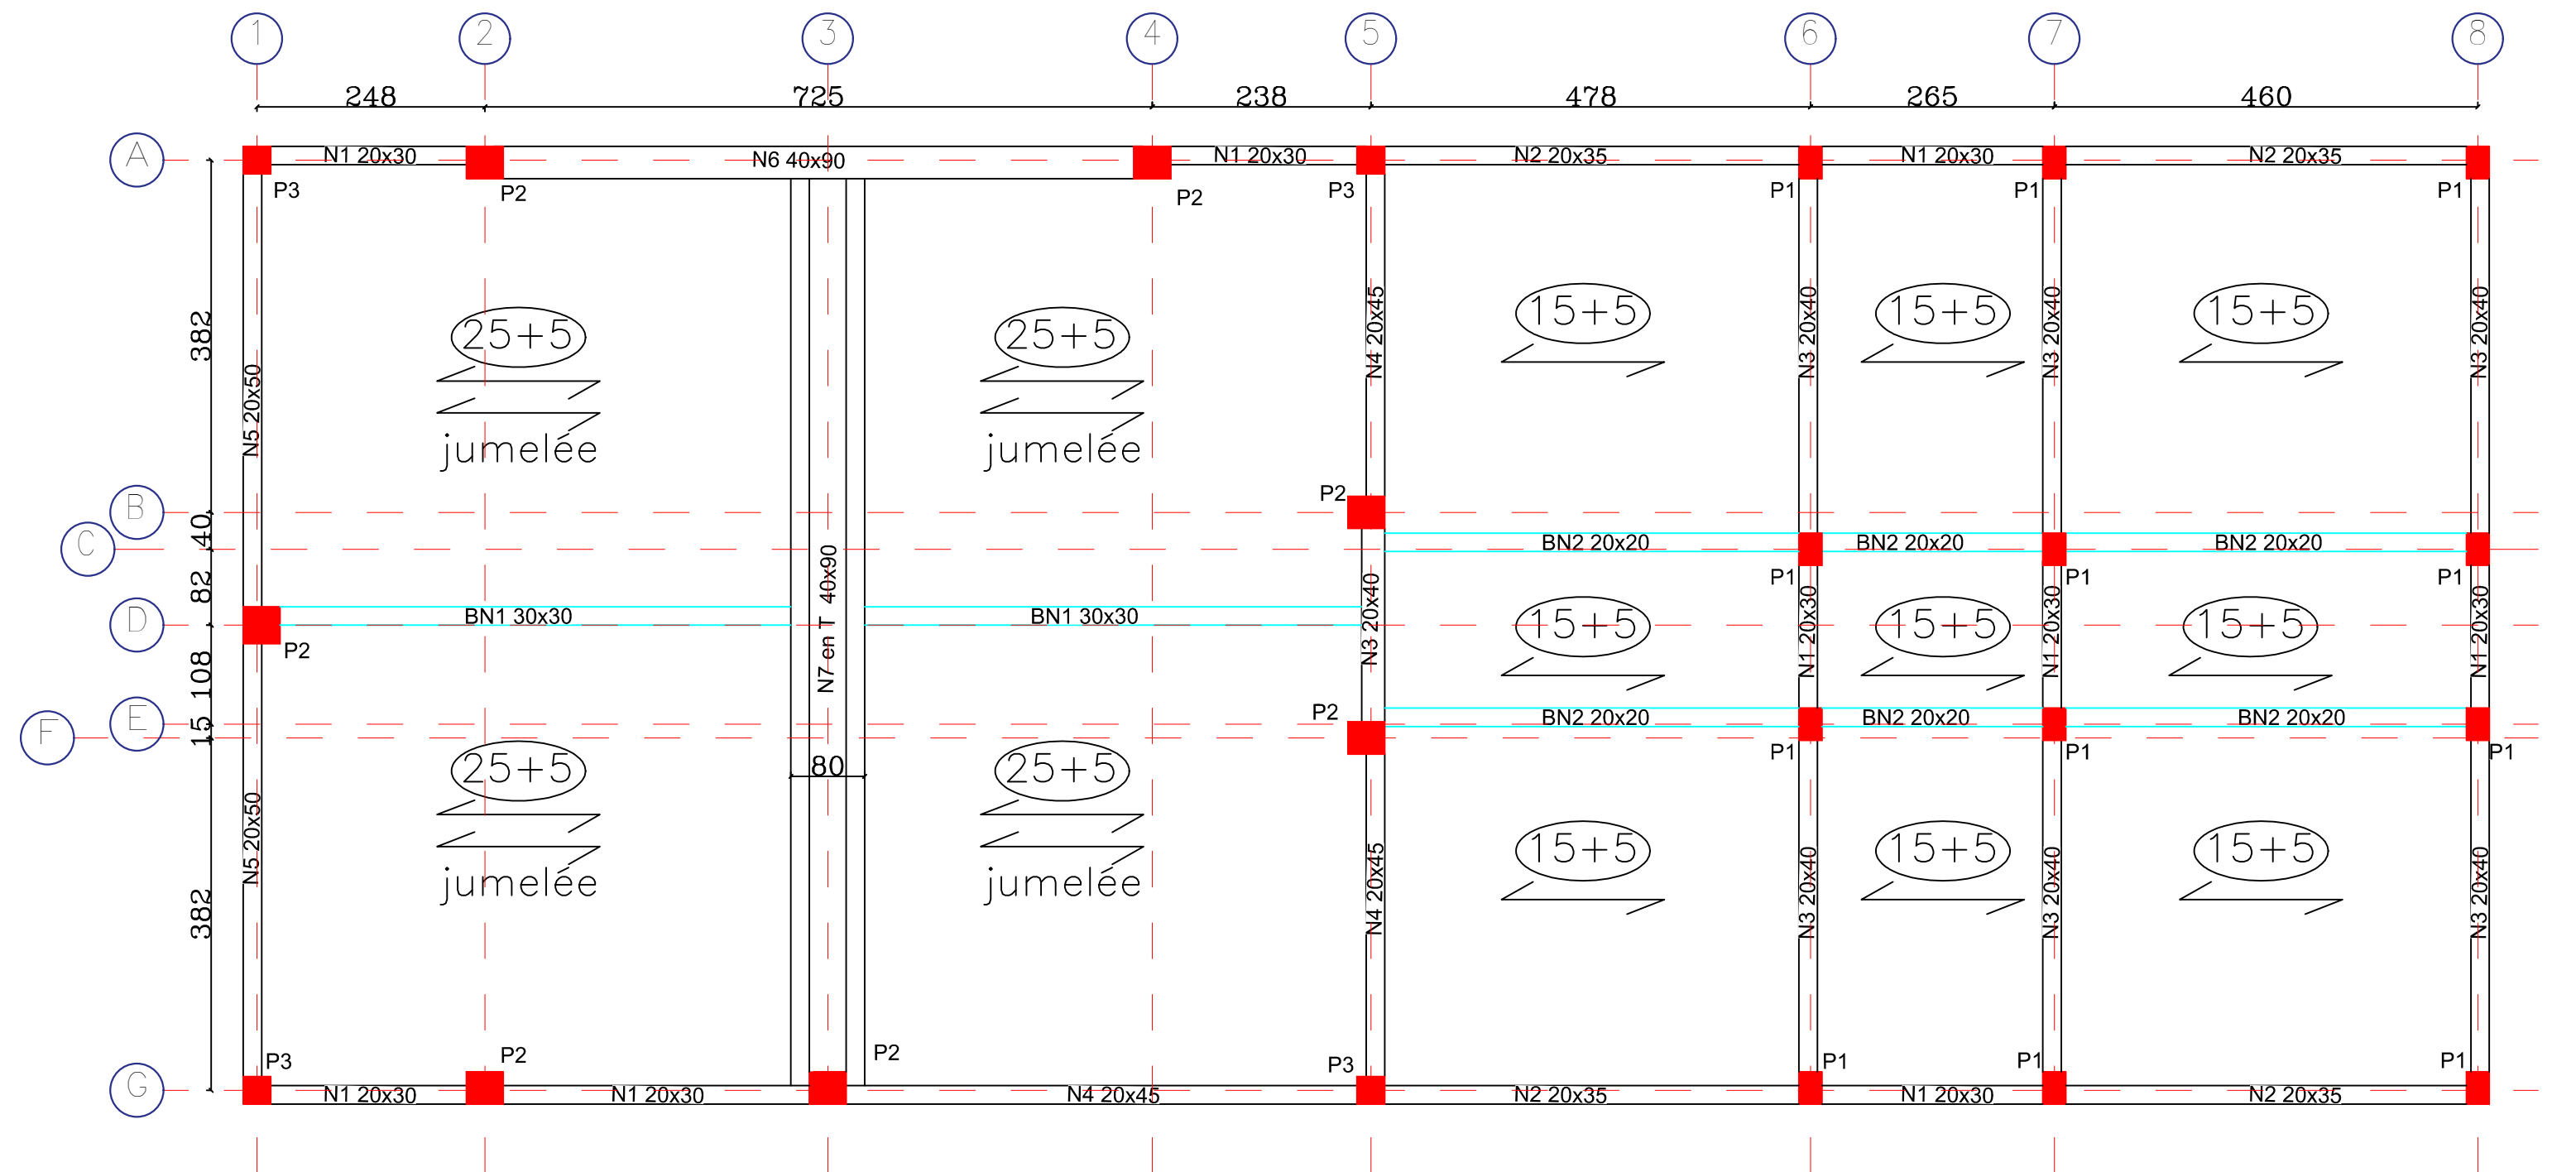
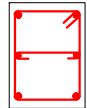
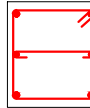
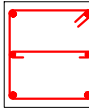
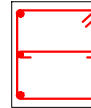
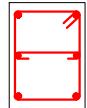
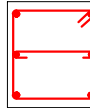
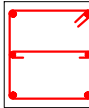
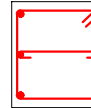


TABLEAU DES POTEAUX

Poteaux Niveaux	P1	P2	P3	P4
mezzanine	(25x35) 6HA14  <u>Cad T6+Ep T6</u> <u>6x8+e=15</u>	(40x40) 6HA14  <u>Cad T6+Ep T6</u> <u>6x8+e=15</u>	(30x30) 6HA14  <u>Cad T6+Ep T6</u> <u>6x8+e=15</u>	(35x35) 6HA14  <u>Cad T6+Ep T6</u> <u>6x8+e=15</u>
PH RDC	(25x35) 6HA14  <u>Cad T6+Ep T6</u> <u>6x8+e=15</u>	(40x40) 6HA14  <u>Cad T6+Ep T6</u> <u>6x8+e=15</u>	(30x30) 6HA14  <u>Cad T6+Ep T6</u> <u>6x8+e=15</u>	(35x35) 6HA14  <u>Cad T6+Ep T6</u> <u>6x8+e=15</u>

DETAIL TYPE POTEAU



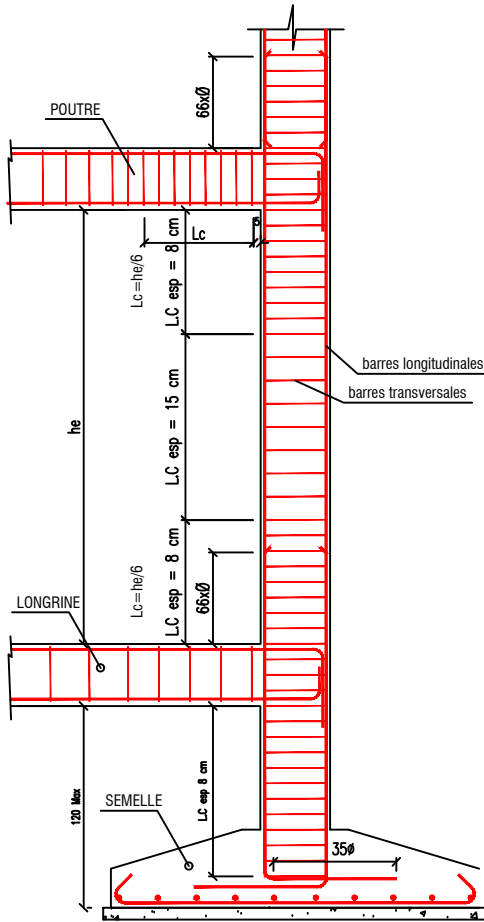


TABLEAU DES SEMELLES

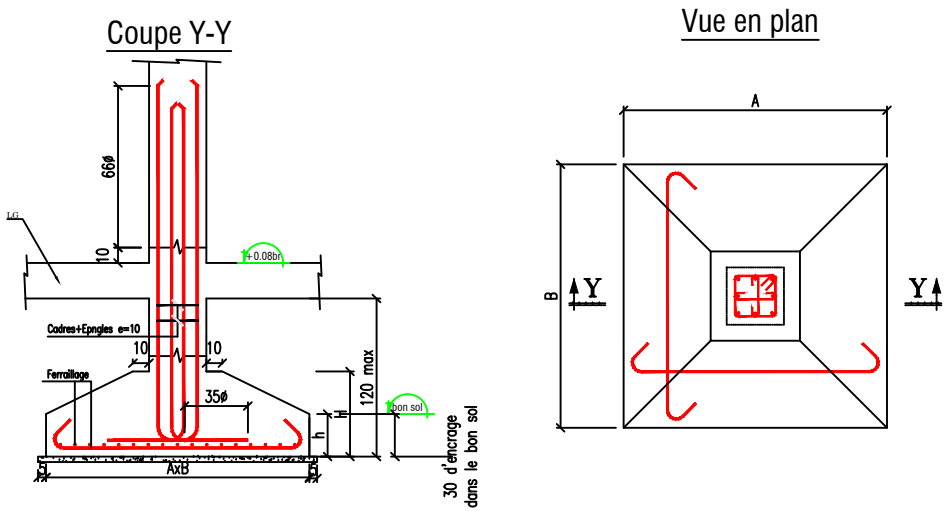


Repère	Dimensions en cm (AxB)	H (cm)	h (cm)	Ferrailage selon x	Ferrailage selon y	Nombre
S1	100x100	25	20	6HA12	6HA12	--
S2	110x110	25	20	7HA12	7HA12	--
S3	120x120	30	20	8HA12	8HA12	--
S4	150x150	40	20	11HA12	11HA12	--

N1
20x30

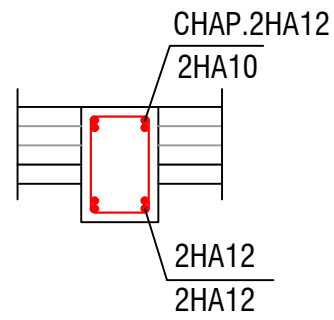


Cad.T6 e=(10x9 const 18 symet)

N2
20x35

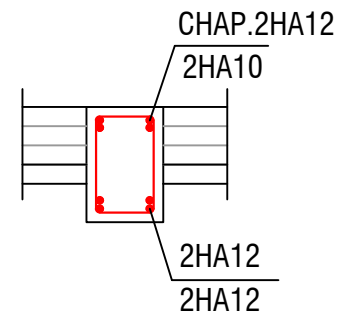


Cad.T6 e=(10x9 const 18 symet)

N3
20x40

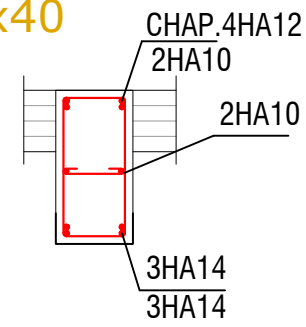


Cad.T6 e=(10x9 const 18 symet)

N4
20x45

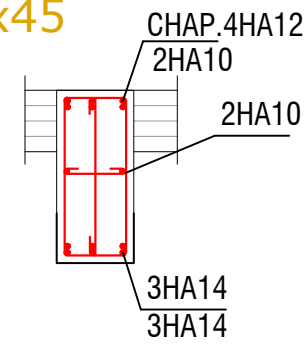


Cad.T6 e=(10x9 const 18 symet)

N5
20x50

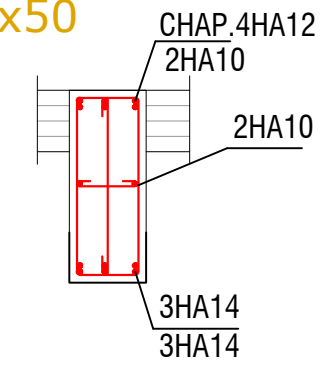


Cad.T6 e=(10x9 const 18 symet)

N7
N630x90
40x90

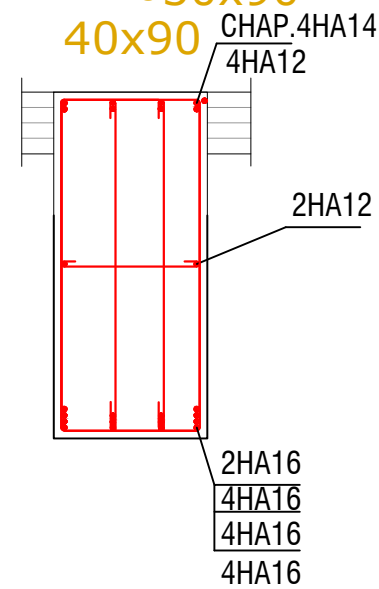


Cad.T6 e=(10x9 const 18 symet)

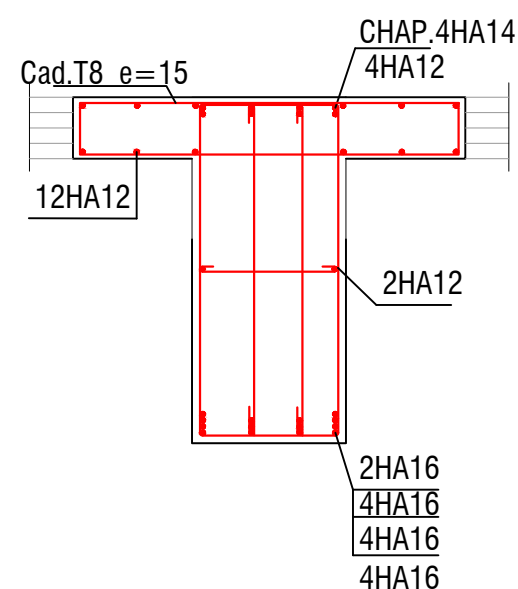


Cad.T6 e=(10x9 const 18 symet)

BN1/BN2

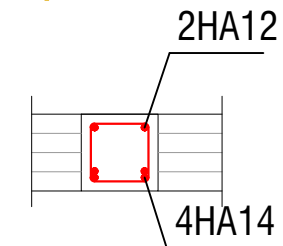


Cad.
e=(9x11 const 18 symet)


DETAIL TYPE POUTRE

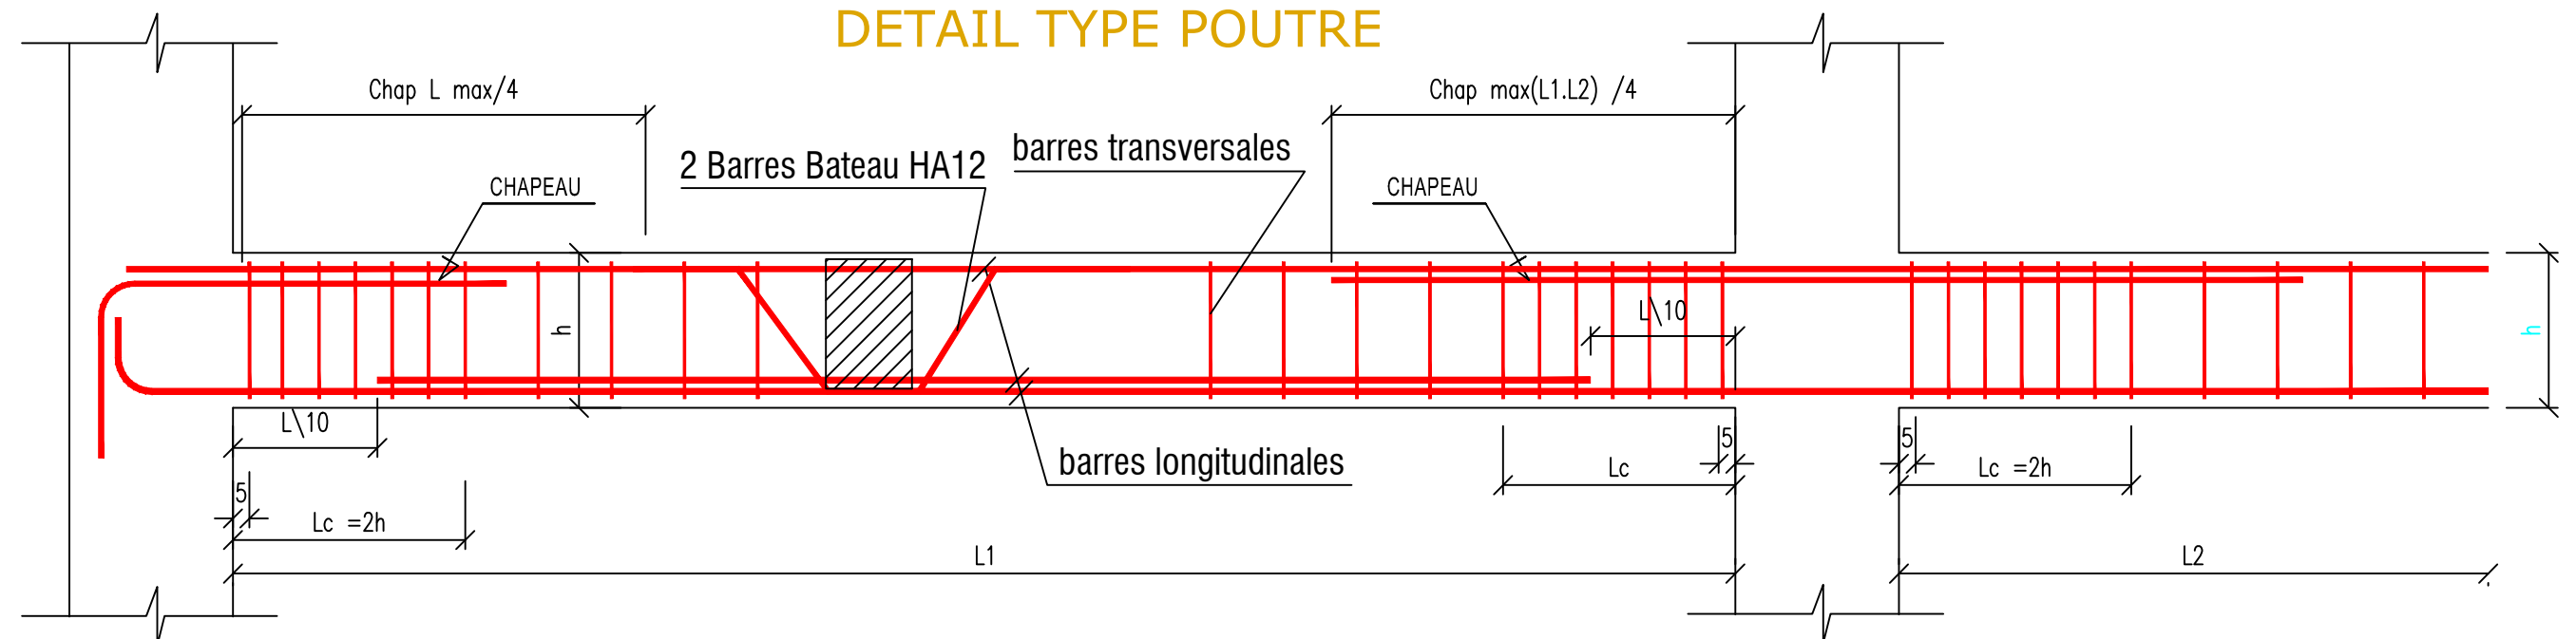


DALLAGE TYPE20

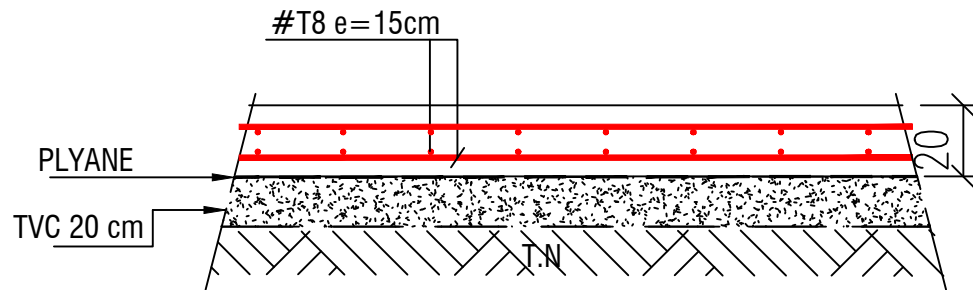


DALLAGE TYPE13

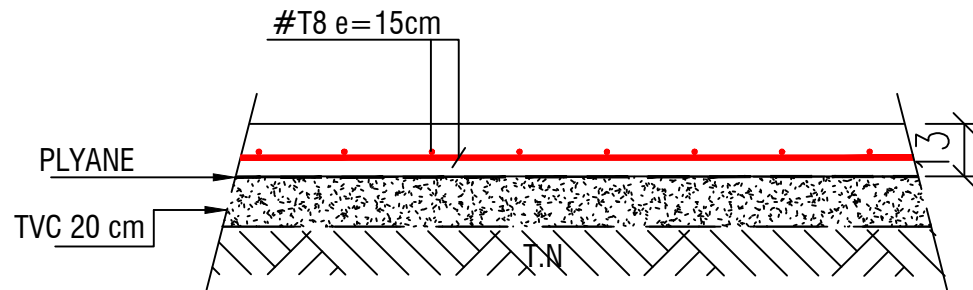


CH (40x20)

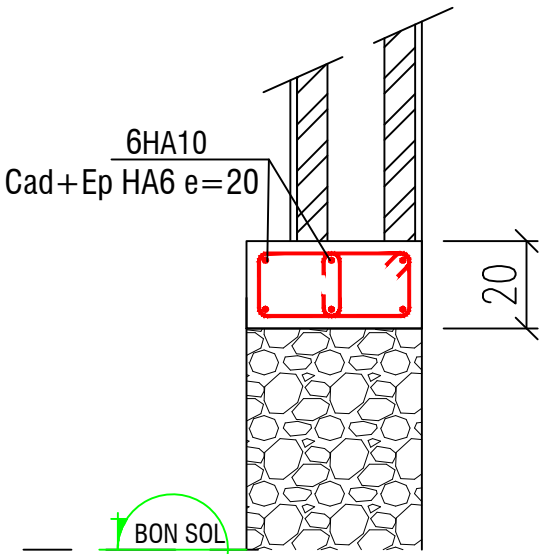

LG1 (20x50)

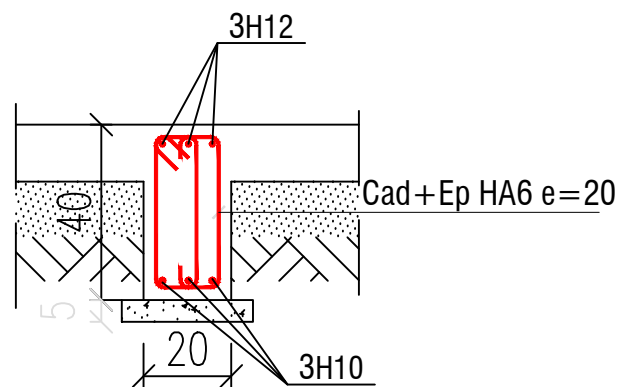

LG (20x40)

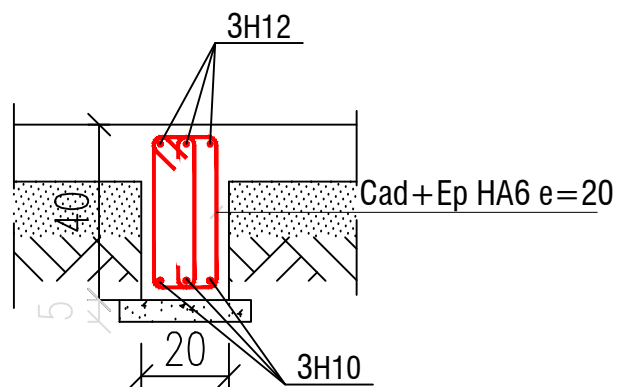

COUPES TYPE ESCALIER

CH2 (20x20)

